

Stromversorgung 5 V (>= 2 A)

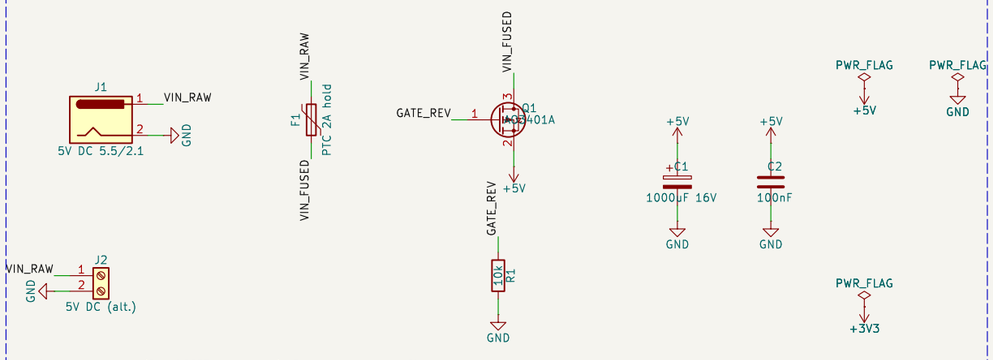


Q1: Verpolschutz (P-MOSFET, high-side). F1: rueckstellende Sicherung.

ESP32-DevKitC V4 (WROOM-32), steckbar

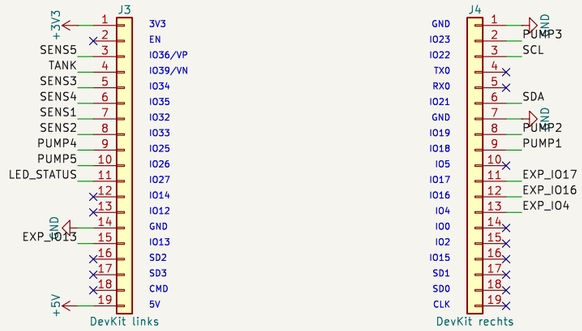


Buchsenleisten 1x19, Reihenabstand 25,4 mm. 3V3 kommt vom DevKit-Regler.


Peripherie

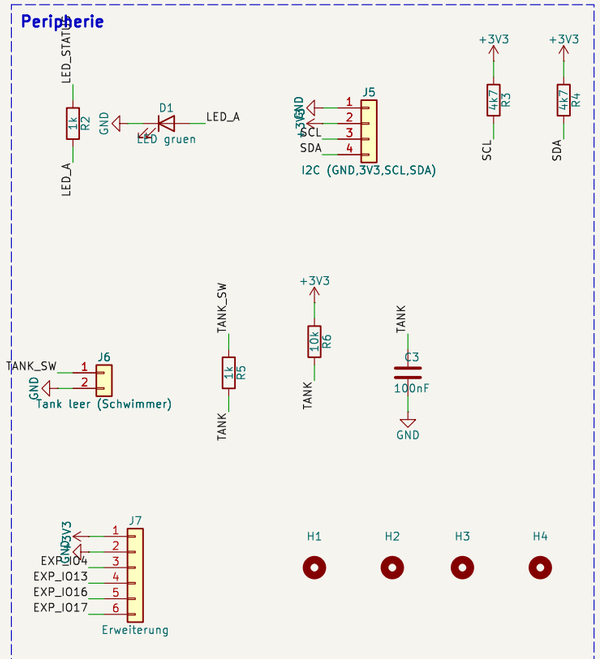

Pumpenkanaele 1-5 (5 V, low-side Logic-Level-MOSFET)

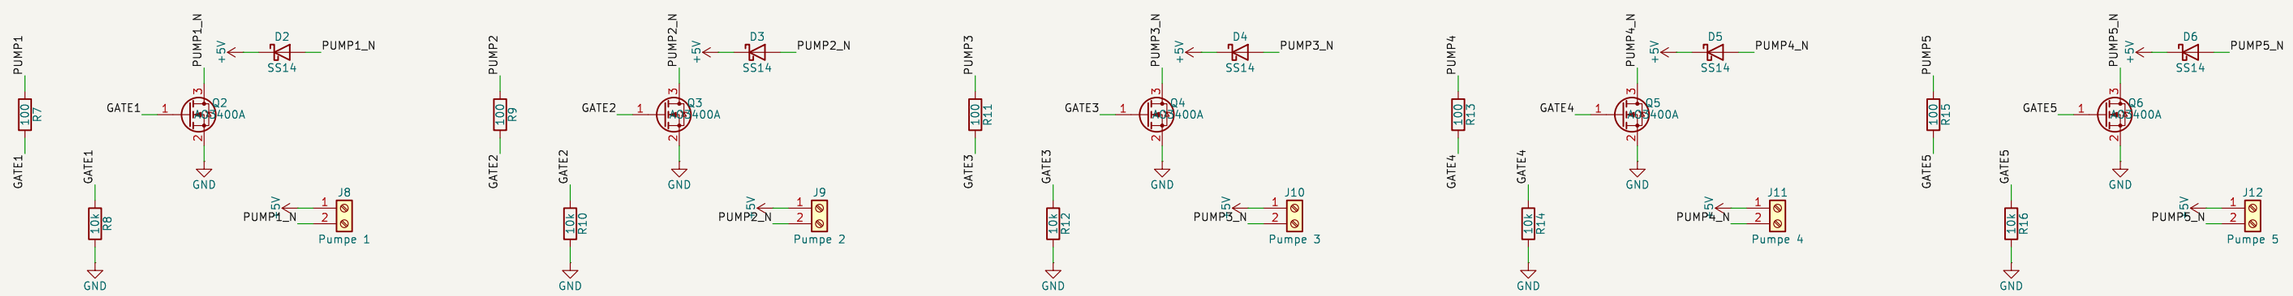

Bodenfeuchtesensoren 1-5 (kapazitiv, 3,3 V, ADC1)

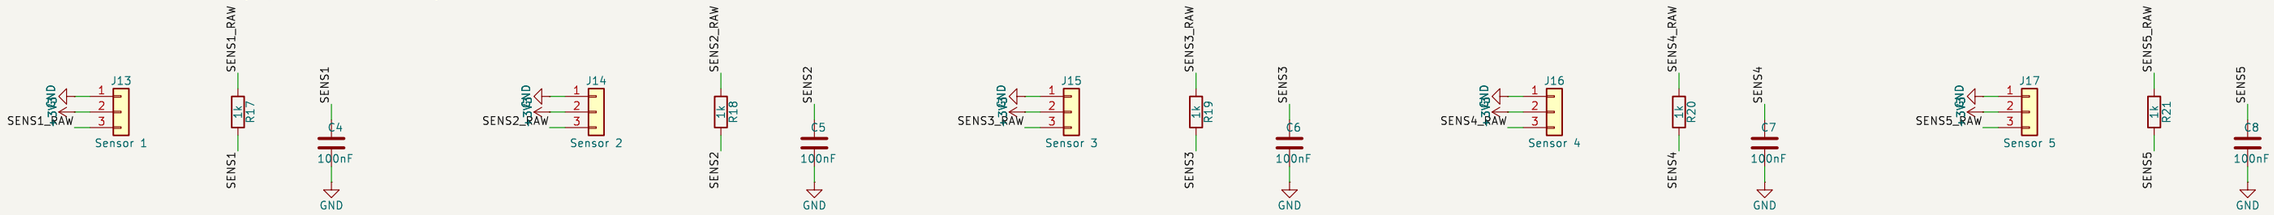

Steckerbelegung wie am Sensor: GND / VCC / AOUT. RC-Tiefpass 1k/100nF gegen Pumpenstoerungen.

Generiert mit hardware/v2/gen_schematic.py – nicht von Hand editieren
ESP32-DevKitC V4, 5x Pumpe, 5x Bodenfeuchte, Tank-Schwimmer, I2C

Balcony Irrigation Project

Sheet: /
File: balcon_irrigation_v2.kicad_sch

Title: Balkonbewaesserung v2 – Steuerplatine

Size: A3	Date: 2026-11-05	**Rev: 0.1**
KiCad E.D.A. 9.0.2		Id: 1/1